


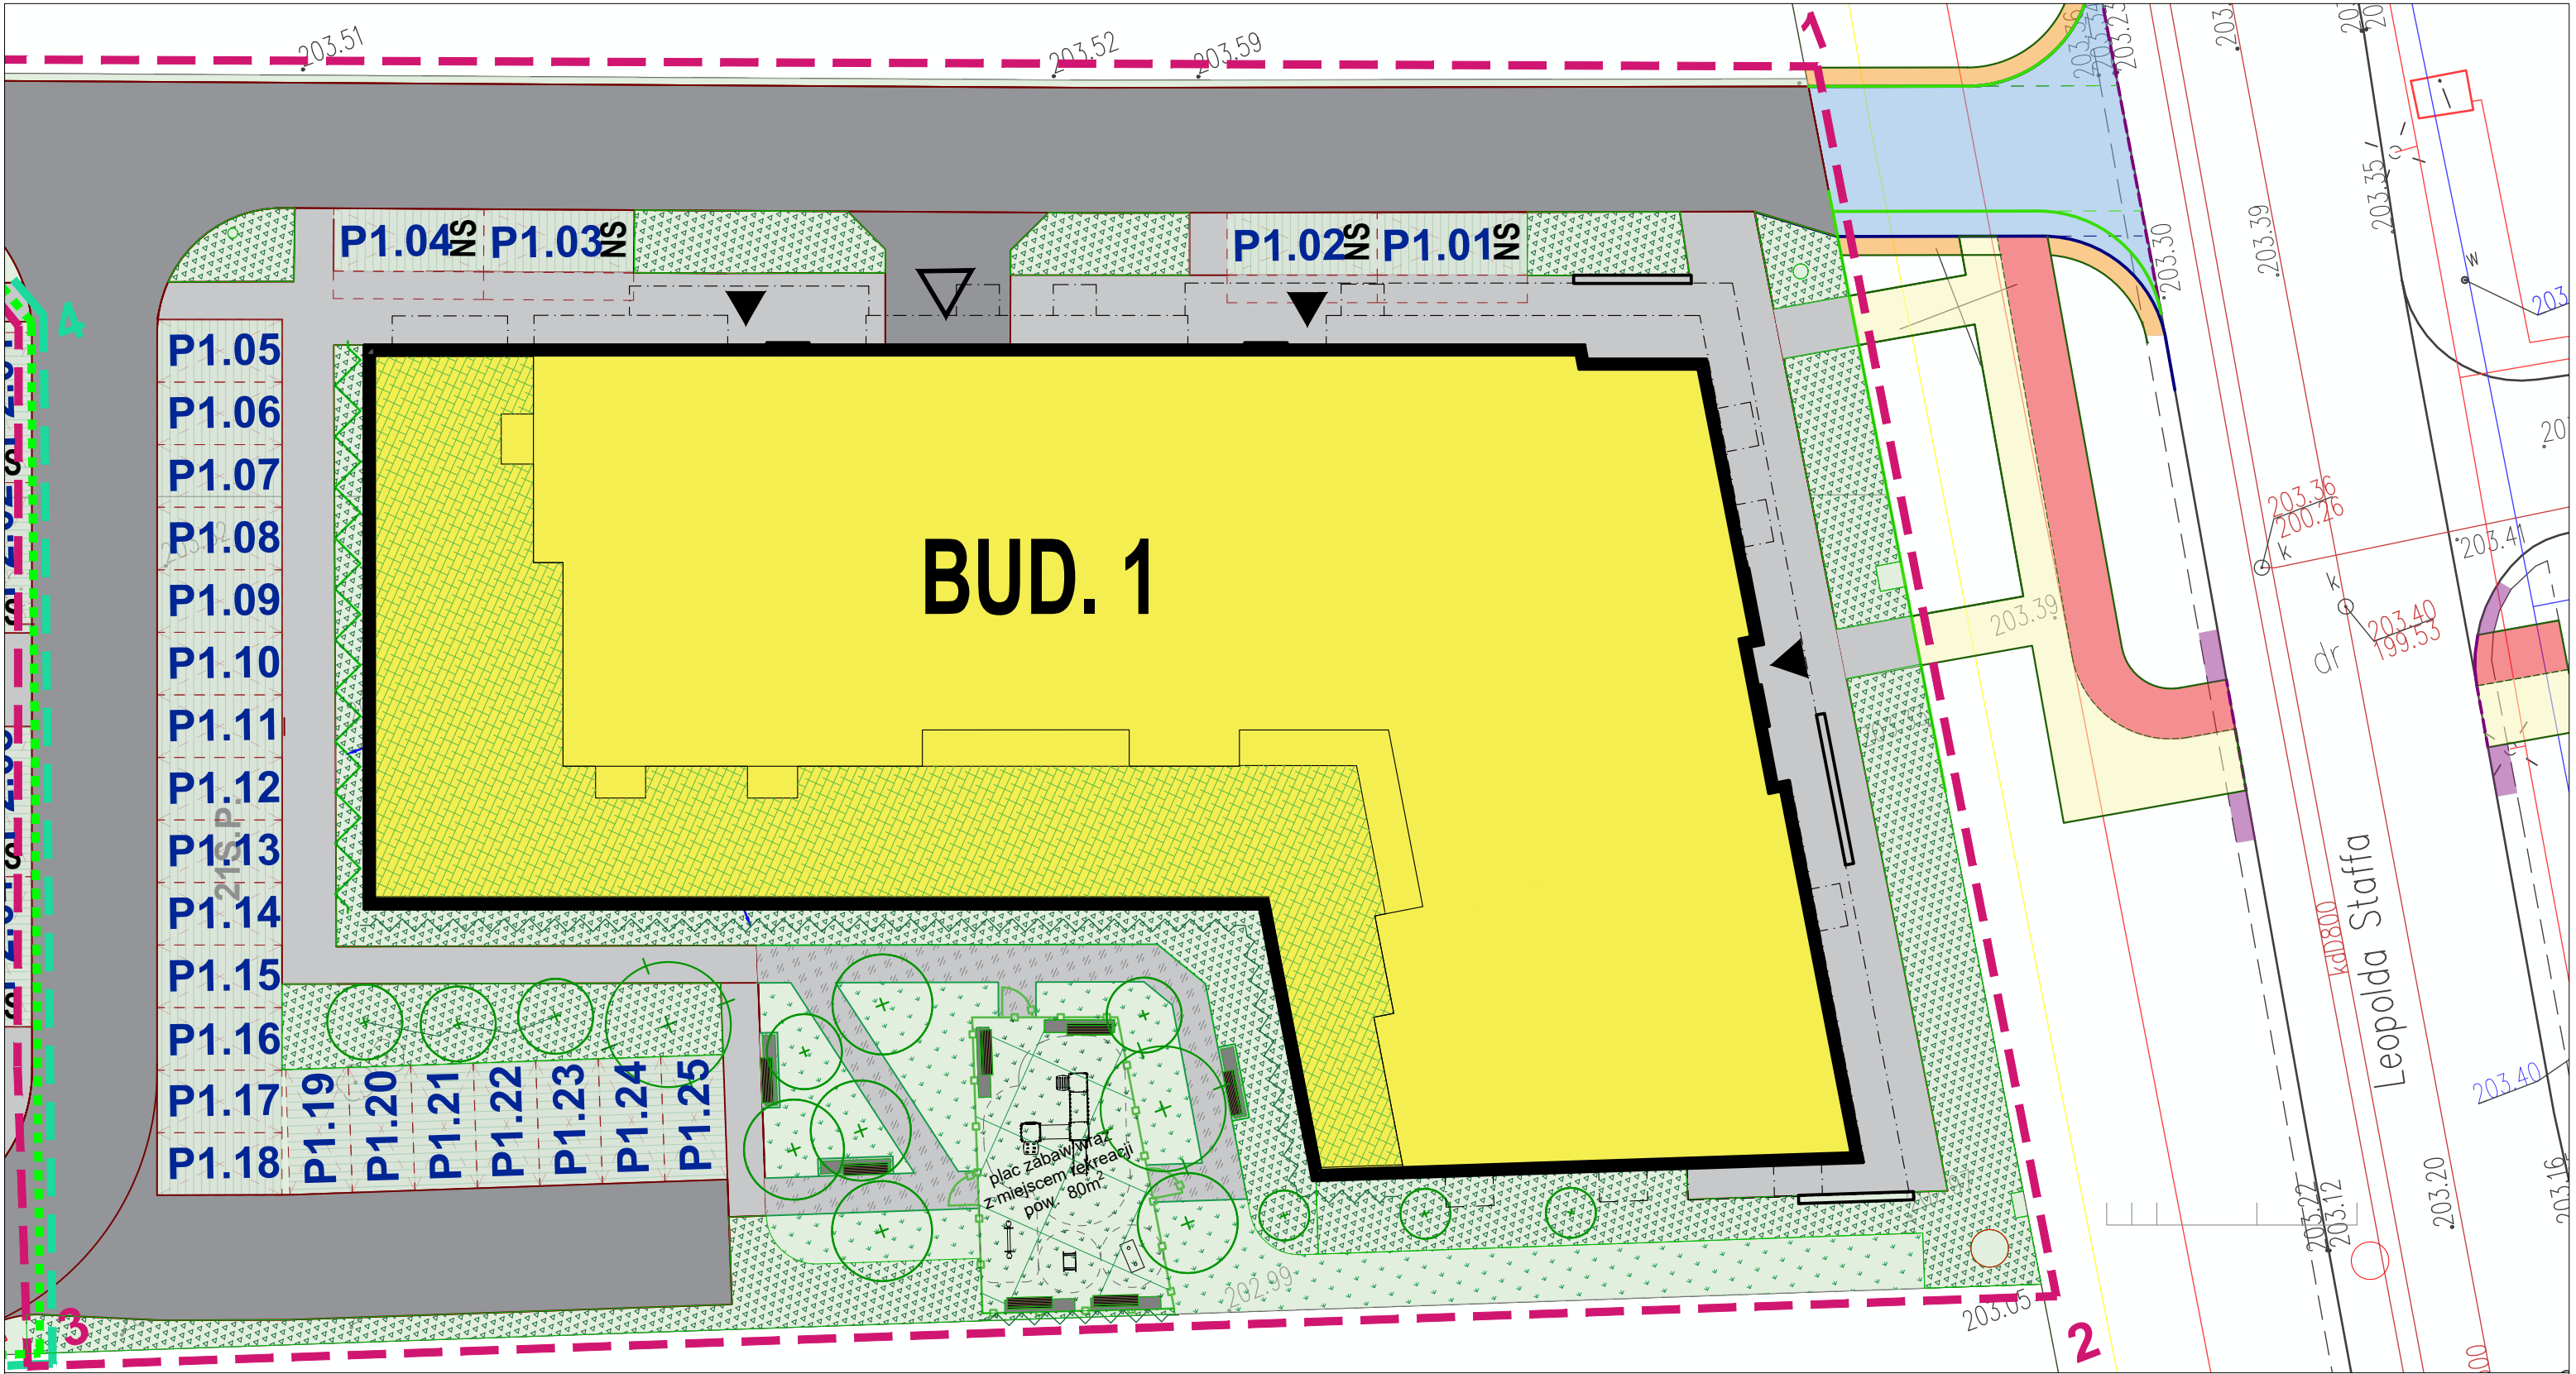

LEGENDA:

- 7B** ZAKRES CAŁEJ INWESTYCJI A,B,C,D,E,F - DZIAŁKI O NR EWID.43/1 ORAZ 44/5 I 44/6 (DAWNIEJ DZIAŁKA NR 44/4)
- 71** ZAKRES NINIEJSZEGO OPRACOWANIA 1-7 - ETAP NR 1- FRAGMENTY DZIAŁEK O NR EWID.43/1 I 44/6
- 71** ZAKRES 1-7 - ETAPY 2-5 - FRAGMENTY DZIAŁEK O NR EWID.43/1 I 44/6 ORAZ DZIAŁKA 44/5, (DAWNIEJ DZIAŁKA NR 44/4) - WG ODRĘBNEGO OPRACOWANIA I ODRĘBNEJ PROCEDURY

- BUD. 1** PROJEKTOWANE BUDYNKI MIESZKALNE WIELORODZINNE Z GARAZAMI W PARTERACH
- 71** PROJEKTOWANE DACHY ZIEŁONE
- 71** PROJEKTOWANE ZADASZENIA I PRZEWIESZENIA BUDYNKU O WYSIĘGU MIN. 1,0m
- BUD. 1** OZNAKOWANIE PROJEKTOWANYCH BUDYNKÓW MIESZKALNYCH WIELORODZINNYCH
- 71** LICZBA KONDYGNACJI
- 71** PROJEKTOWANE WEJŚCIE DO BUDYNKU
- 71** PROJEKTOWANY WJAZD DO GARAŻU WIELOSTANOWISKOWEGO ZLOKALIZOWANO W PARTERACH BUDYNKÓW
- 71** PROJEKTOWANE TRAWNIKI / ZIELEŃ NISKA

- 71** PROJEKTOWANE PLACE ZABAW WRAZ Z MIEJSCEM REKREACJI
- 71** PROJEKTOWANA NAWIERZCHNIA UTWARDZONA Z KOSTKI BETONOWEJ
- 71** PROJEKTOWANA NAWIERZCHNIA UTWARDZONA Z PŁYT AZUROWYCH np. BETARD ECOGRATTA (współczynnik pow. biologicznie czynnej równy 48%) LUB RÓWNOWAŻNY
- 71** PROJEKTOWANA NAWIERZCHNIA UTWARDZONA Z PŁYT AZUROWYCH np. geoSYSTEM G4 MAX (współczynnik pow. biologicznie czynnej równy 86%) LUB RÓWNOWAŻNY
- 71** PROJEKTOWANA NAWIERZCHNIA ŻWIROWA
- 71** PROJEKTOWANA ZIELEŃ ŚREDNIOWYSOKA I WYSOKA
- 71** PROJEKTOWANA ZIELEŃ DO MAKSYMALNEJ WYSOKOŚCI 3,0m

- 71** ISTNIEJĄCE DRZEWIA - PAS ZIELENI IZOLACYJNEJ
- 71** PROJEKTOWANA DRZEWIA LIŚCIASTE WG ODRĘBNEGO OPRACOWANIA
- 71** PROJEKTOWANE DRZEWIA IGŁASTE WG ODRĘBNEGO OPRACOWANIA
- 71** PROJEKTOWANA ZIELEŃ NISKA WG ODRĘBNEGO OPRACOWANIA -KRZEWY I BYLINY
- 71** PROJEKTOWANY TRAWNIK WG ODRĘBNEGO OPRACOWANIA
- 71** PROJEKTOWANY TRAWNIK NA MACIE PRZEROSTOWEJ WG ODRĘBNEGO OPRACOWANIA

- 71** OZNACZENIE PROJEKTOWANYCH MIEJSC POSTOJOWYCH O WYM. 2,50x5,00m / 2,50x6,00m
- 71** OZNACZENIE PROJEKTOWANYCH MIEJSC POSTOJOWYCH DLA OSÓB NIEPEŁNOSPRAWNYCH O WYM. 3,60x5,00m
- 71** OZNACZENIE PROJEKTOWANYCH MIEJSC POSTOJOWYCH DLA OSÓB NIEPEŁNOSPRAWNYCH O WYM. 2,50x6,00m Z ZAPEWNIONYM DOJŚCIEM O SZER. 1,10m
- P1.02** NUMER PROJEKTOWANYCH MIEJSC POSTOJOWYCH

0 1 2 5 10 m